

TRACT NO. 20429

IN UNINCORPORATED TERRITORY OF LOS ANGELES COUNTY, CALIFORNIA.
BEING A SUBDIVISION OF A PORTION OF LOT "H" PARTITION OF THE RANCHO LOS PALOS VERDES ALLOTTED TO JOTHAM BIXBY BY DECREE OF PARTITION IN ACTION: BIXBY ET AL VS BENT ET AL CASE NO 2373 IN THE DISTRICT COURT OF THE 17th JUDICIAL DISTRICT OF THE STATE OF CALIFORNIA, IN AND FOR THE COUNTY OF LOS ANGELES: ENTERED IN BOOK 4 AT PAGE 57 OF JUDGMENTS IN THE SUPERIOR COURT OF SAID COUNTY. CLERKS FILED MAP NO. 4, RECORDS OF LOS ANGELES COUNTY.

Aug. 31, 1955
41 3 P.M.
574
31

I hereby certify that I am a Registered Civil Engineer of the State of California, that this map consisting of two sheets correctly represents a true and complete survey made under my supervision in February 1955, that the monuments of the character and location shown hereon will be in place not later than August 1, 1956, that said monuments are sufficient to enable the survey to be readily retraced and that tie notes to all center-line monuments shown hereon as set by me will be on file in the office of the County Engineer not later than September 1, 1956.

Charles C. Miller
Registered Engineer No. 122

We hereby certify that we are the owners of or are interested in the lands included within the subdivision shown on this map within the colored border lines, and we consent to the preparation and recordation of said map and subdivision and hereby dedicate to the public use all Streets, Highways and other public ways shown on said map and also grant to the County of Los Angeles the easements for storm drain purposes so designated on said map and all uses incident thereto, including the right to make connections therewith from any adjoining properties, and also grant to the County of Los Angeles the slope easement shown on said map. We further certify that, except as shown on a copy of this map on file in the office of the County Road Commissioner, we know of no easements or structures existing within the easements hereby offered for dedication to the public, other than publicly owned water lines, sewers, or storm drains, that we will grant no right or interest within the boundaries of said easements offered to the public, except where such right or interest is expressly made subject to the said easements.

We hereby offer to the public use the private streets shown on said map which shall have ceased to remain closed or posted and shall have been opened to the public travel for a period of three months or more. As a dedication to public use, while all of Narbonne Avenue within this subdivision remains a public highway, and for such time only, we hereby abandon all easements of vehicular ingress and egress to the said Narbonne Avenue, except through the private streets shown as shown on said map, so that owners of lots abutting Narbonne Avenue during such time will have no rights of access whatever in the highway as such except the general easement of travel which belongs to the whole public. If any change of alignment or width of such highway results in the vacation of any part thereof within this subdivision, such vacation terminates the above dedication as to the part vacated.

In re Acceptance of Highways, Public Ways, etc.
TRACT NO 20429
The Board of Public Works of the County of Los Angeles, California, do hereby certify that the map and the same is hereby approved, that the bond filed in the office of this Board as security for the payment of taxes and special assessments collected as taxes be and the same is hereby approved in the sum of \$1,125.00 which is hereby fixed as the amount of said bond and that all streets, highways, other public ways shown on said map and thereon offered for dedication be and the same are hereby accepted on behalf of the public. Also the offer of dedication for abandonment of ingress and egress is hereby accepted. And the Private Street shown on said map and herein offered for dedication is hereby rejected under provisions of Section 11616 of the Subdivision Map Act.

Mame B. Beatty
L. Jargubar
\$3.00

The Clerk of this Board is directed to see this order authenticated by the Seal of the Board and to file the same in the office of the County Clerk of said County. August 30, 1955
Harold J. Ostly
County Clerk of Los Angeles County

I hereby certify that I have examined this map; that it conforms substantially to the tentative map and all approved alterations thereof; that all provisions of applicable State law and local subdivision ordinances have been complied with; and that I am satisfied that this map is technically correct.
August 31, 1955
WILLIAM J. FOX
COUNTY ENGINEER
By Harold Kennedy Deputy

INSTITUTE OF ESOTERIC PHILOSOPHY A Corporation
Irwin Palmer President
Alma Bright Secretary

James H. Cornell Jr.
Sally S. Cornell
Lorne M. Burrell
Emmett R. Burrell
as owners and as holders of an appurtenant easement recorded as O.R. 46798-232

CALIFORNIA BANK (a corporation) successor in interest to California Trust Company (a corporation)
Trustee under deed of trust recorded as O.R. 34516-436
Daniel S. Rolph Vice President
H. W. Koch Assistant Secretary


TITLE INSURANCE AND TRUST COMPANY (a corporation)
Trustee under deeds of trust recorded as O.R. 45347-229, O.R. 45348-231, & O.R. 47119-392
Wm. J. Fox Vice President
E. A. J. J. J. Asst Secretary

STATE OF CALIFORNIA } S.S.
COUNTY OF LOS ANGELES }
On this 6 day of April in the year of 1955 before me, the undersigned, a notary public in and for said county, personally appeared Irwin Palmer known to me to be the President and Alma Bright known to me to be the Secretary of the Institute of Esoteric Philosophy the corporation that executed the within instrument and known to me to be the persons who executed the within instrument on behalf of the corporation herein named and acknowledged to me that they executed the same. IN WITNESS WHEREOF I have hereunto set my hand and affixed my official seal the day and year in this certificate first above written.
Lorne M. Burrell
Notary Public in and for said County and State
My Commission expires June 21, 1958

STATE OF CALIFORNIA } S.S.
COUNTY OF LOS ANGELES }
On this 27th day of April in the year 1955 before me, the undersigned, a notary public in and for said county, personally appeared James H. Cornell Jr., Sally S. Cornell, Emmett R. Burrell, & Lorne M. Burrell known to me to be the persons whose names are subscribed to the within instrument and acknowledged to me that they executed the same. IN WITNESS WHEREOF I have hereunto set my hand and affixed my official seal the day and year in this certificate first above written.
E. A. J. J. J.
Notary Public in and for said County and State
My Commission expires May 21, 1955

STATE OF CALIFORNIA } S.S.
COUNTY OF LOS ANGELES }
On this 2nd day of May in the year of 1955 before me, the undersigned, a notary public in and for said county, personally appeared Samuel S. Rolph known to me to be the Vice President and H. W. Koch known to me to be the Assistant Secretary of California Bank the corporation that executed the within instrument and known to me to be the persons who executed the within instrument on behalf of the corporation herein named and acknowledged to me that they executed the same as trustee. IN WITNESS WHEREOF I have hereunto set my hand and affixed my official seal the day and year in this certificate first above written.
Adrian F. Brooks
Notary Public in and for said County and State
My Commission expires March 27, 1957

STATE OF CALIFORNIA } S.S.
COUNTY OF LOS ANGELES }
On this 2nd day of May 1955 in the year of 1955 before me, the undersigned, a notary public in and for said county, personally appeared Clara Cammer known to me to be Vice President and H. W. Koch known to me to be the Assistant Secretary of Title Insurance and Trust Company the corporation that executed the within instrument and known to me to be the persons who executed the within instrument on behalf of the corporation herein named and acknowledged to me that they executed the same as trustee. IN WITNESS WHEREOF I have hereunto set my hand and affixed my official seal the day and year in this certificate first above written.
D. E. Danilack
Notary Public in and for said County and State
My Commission expires Feb 26, 1956

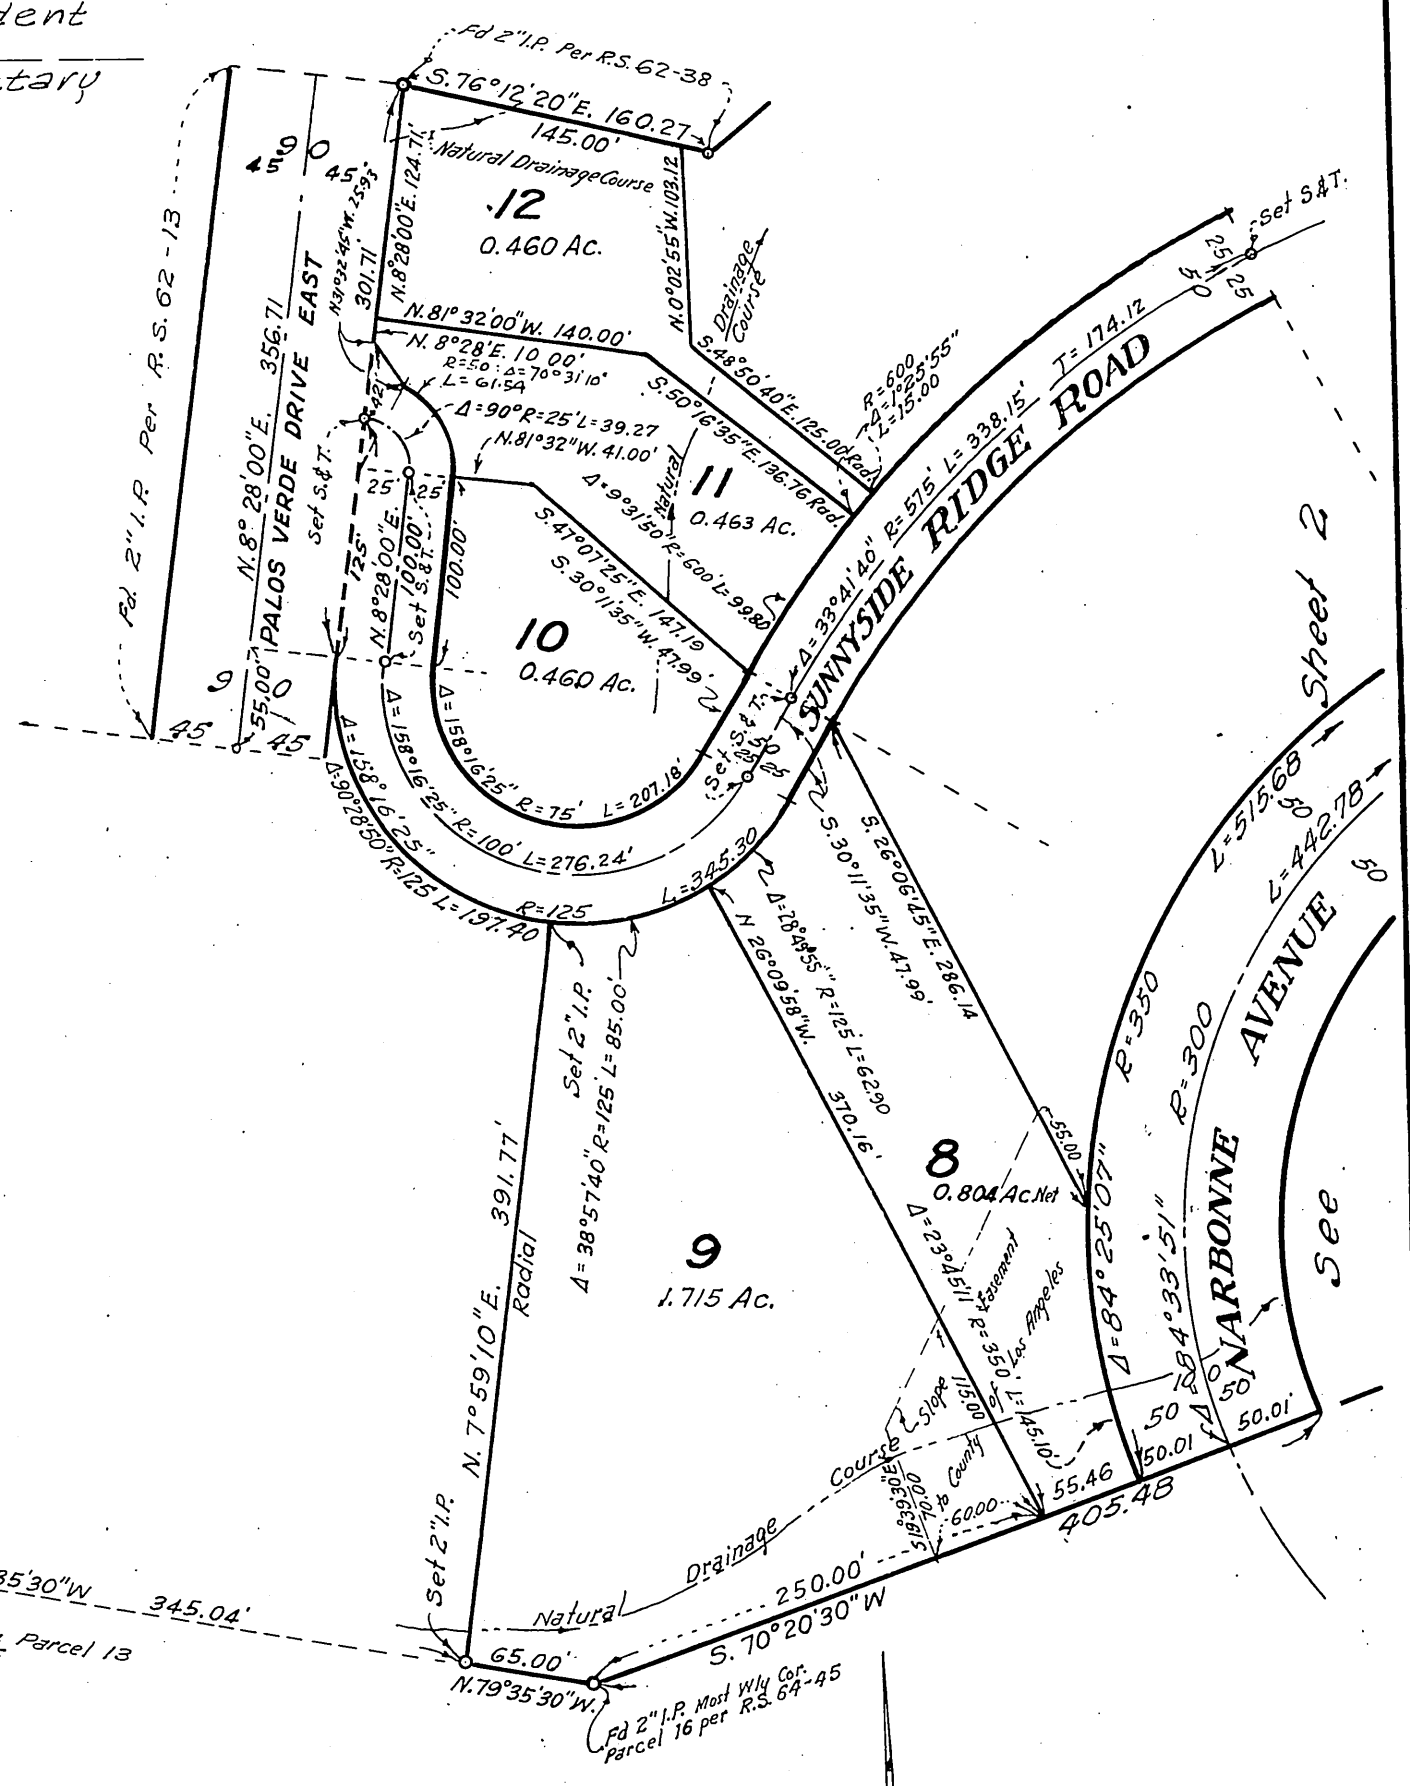


Bearings shown hereon are based on the bearing S 8° 28' 00" W as shown in E of Palos Verde Drive East on R.S. 62-13
All 2" I.P. shown as set hereon are 6" to 8" below ground surface

TRACT NO. 20429

Aug. 31, 1935
K.I.
3 P.M.
574
32

L. Darguham
Free

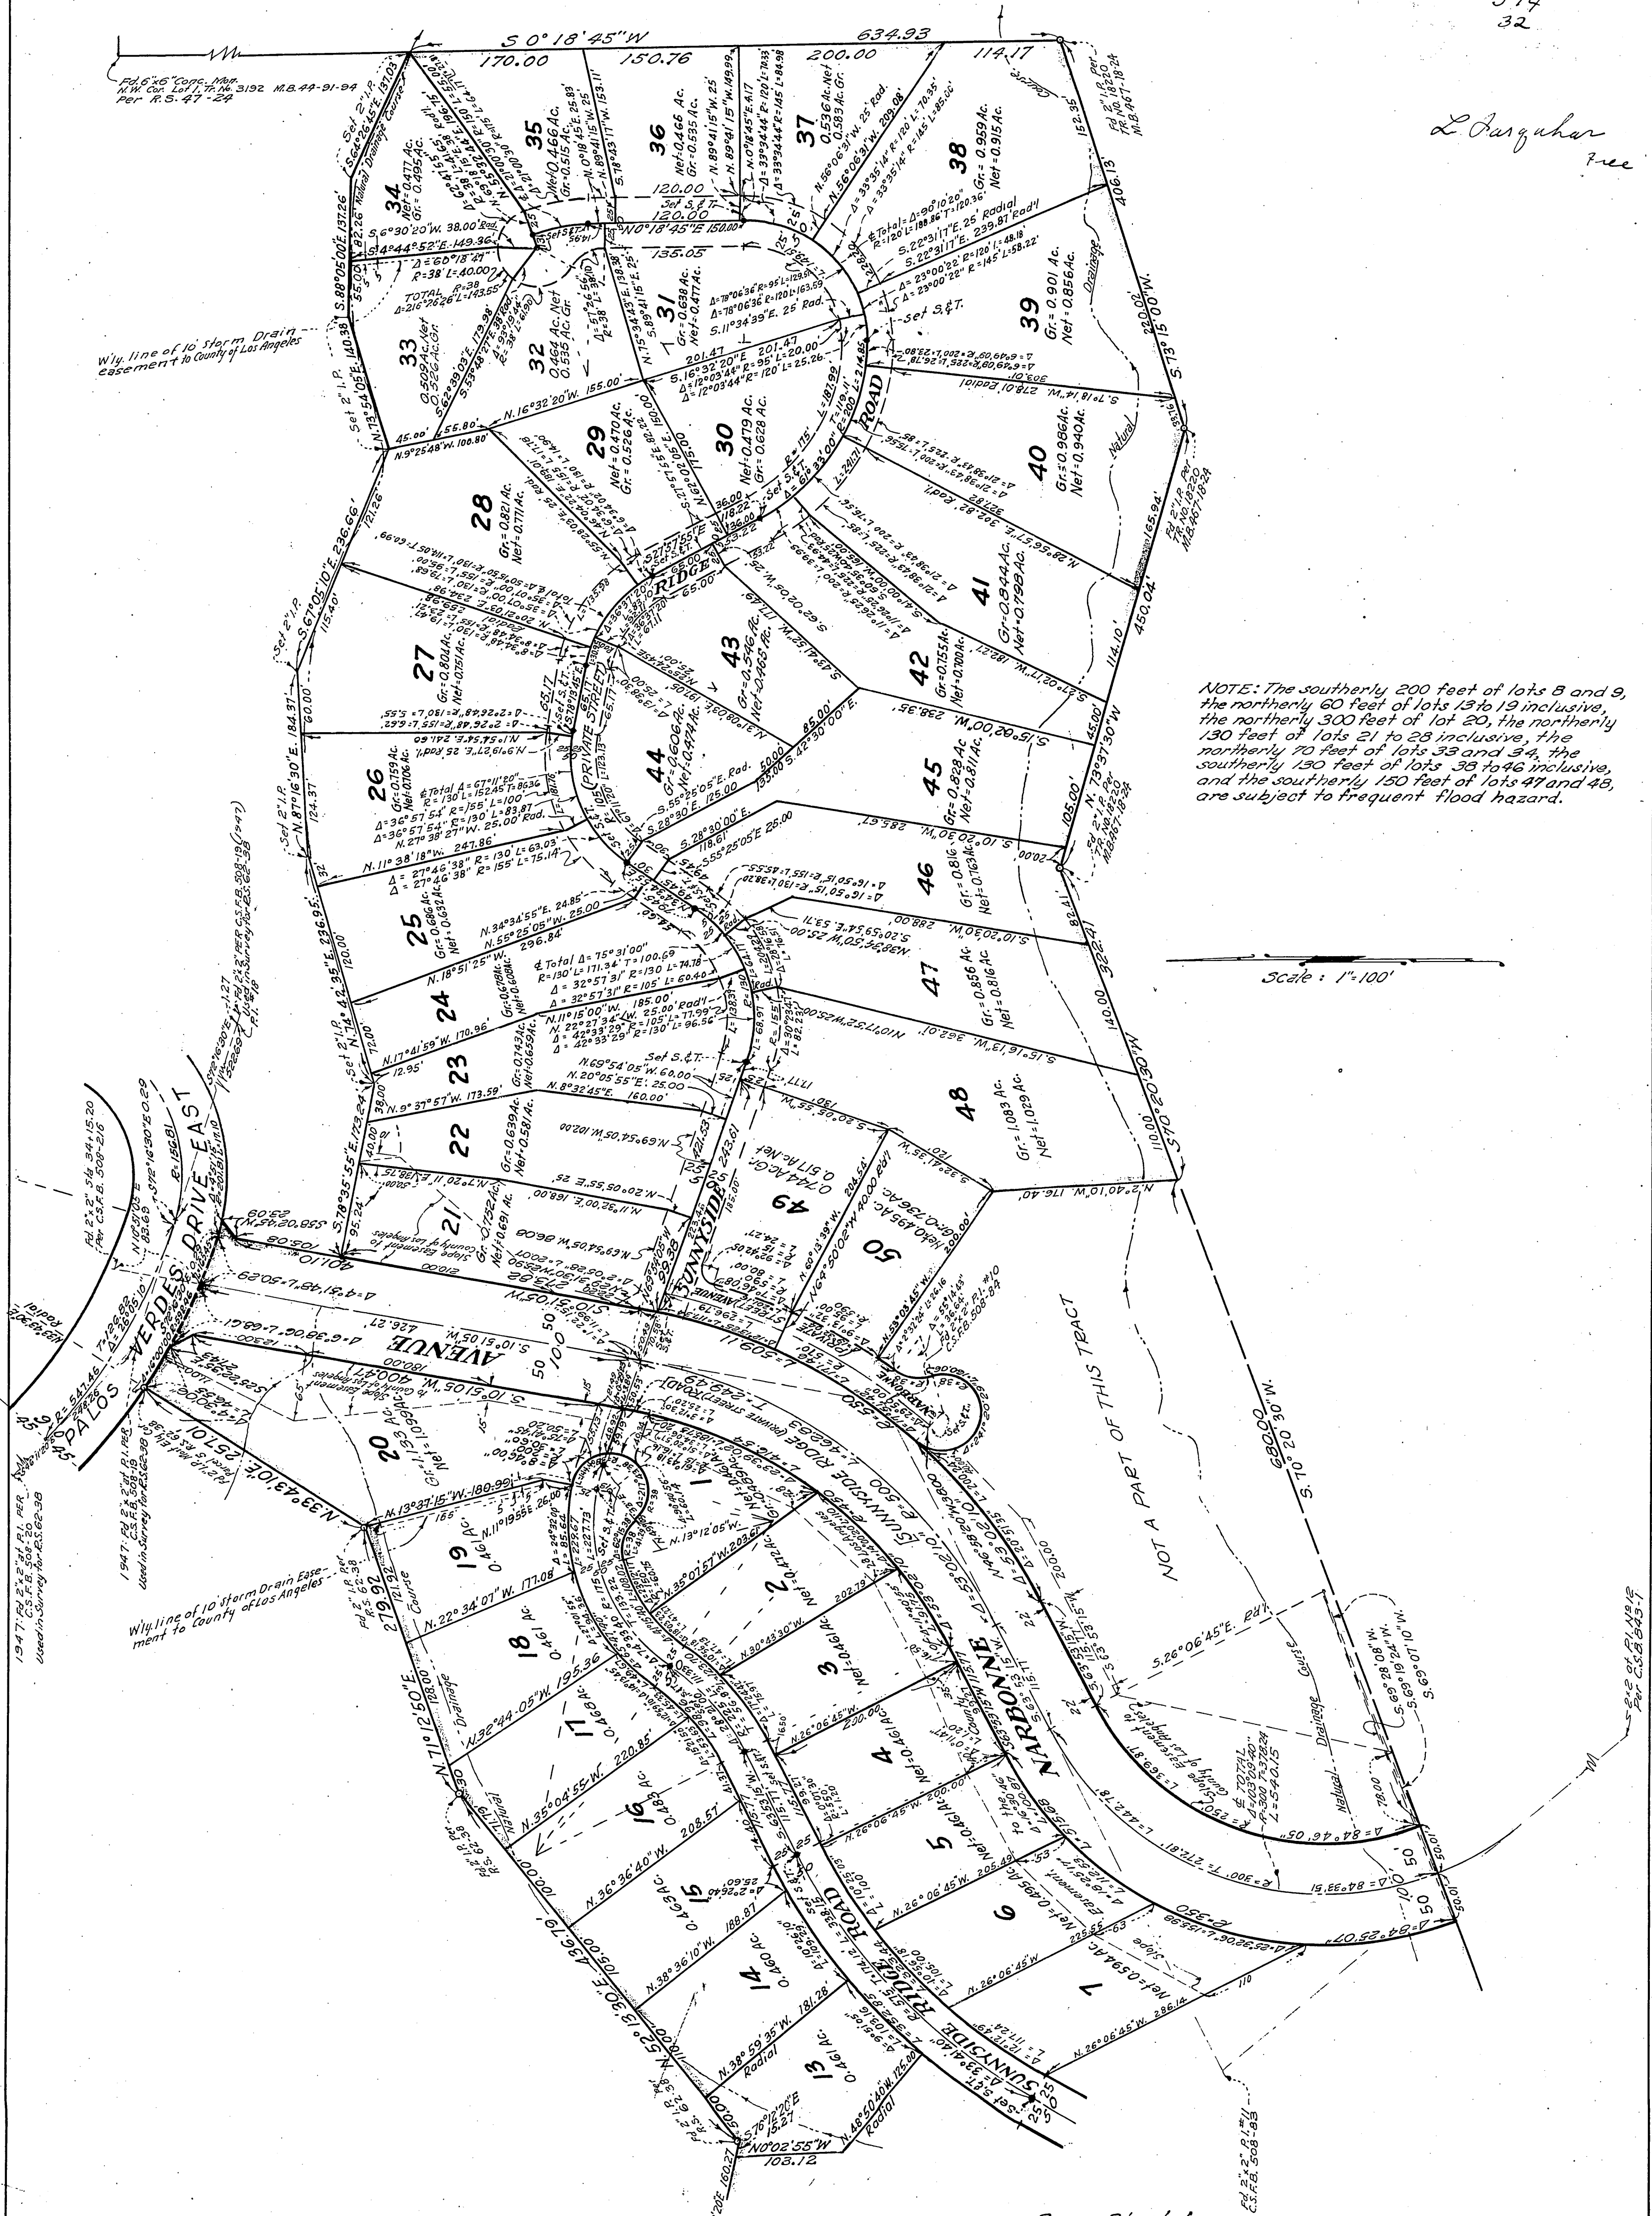

NOTE: The southerly 200 feet of lots 8 and 9, the northerly 60 feet of lots 13 to 19 inclusive, the northerly 300 feet of lot 20, the northerly 130 feet of lots 21 to 28 inclusive, the northerly 70 feet of lots 33 and 34, the southerly 130 feet of lots 38 to 46 inclusive, and the southerly 150 feet of lots 47 and 48, are subject to frequent flood hazard.

See Sheet 1